

PRICE SCOPE: only the Nudura ICF formwork and associated accessories are included in our price. All other structure and information shown is supplied in good faith for coordination only and must be checked by the relevant professional.

QUOTATION - NOT FOR CONSTRUCTION

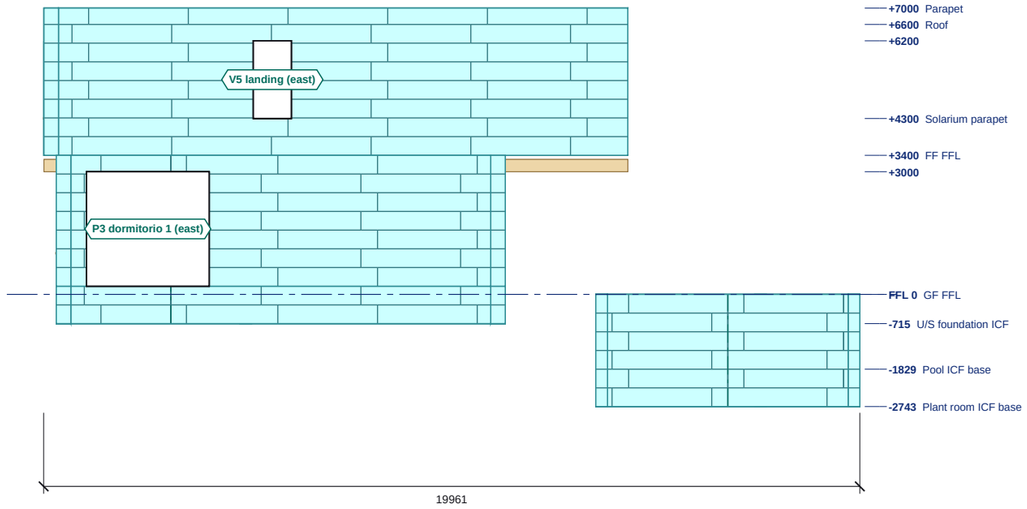

EAST ELEVATION

Scale 1:150 @ A3 | Levels above GF FFL; sills and heads in the schedule

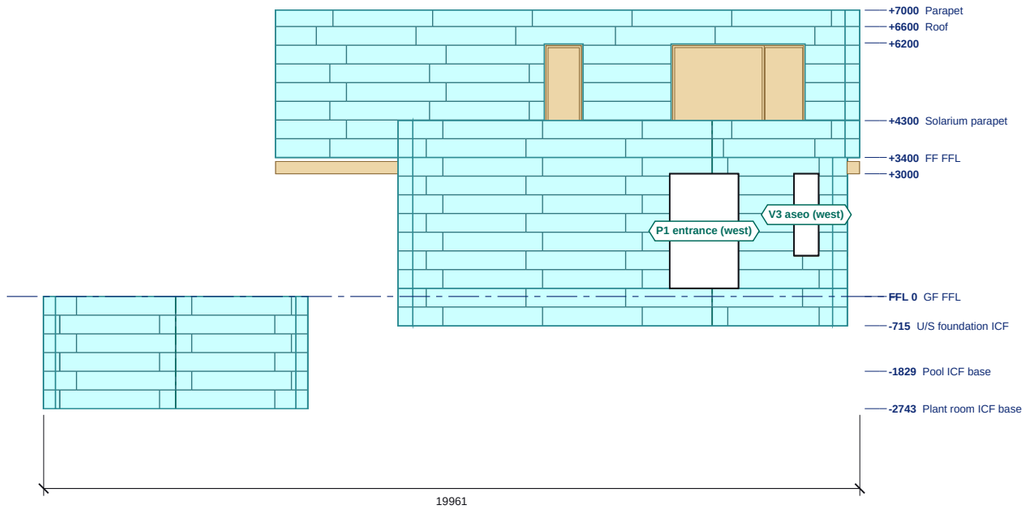

WEST ELEVATION

Scale 1:150 @ A3 | Levels above GF FFL; sills and heads in the schedule

0 1 2 3 4 5 6 7 8m

ICF external EPS face
Block course joint
Stack joint
Roof build-up (slab / earth / sedum)

Do not scale. All dimensions in millimetres, levels in metres from GF FFL. Check all dimensions on site.

ELEVATION SCHEDULES

EAST ELEVATION: OPENINGS

Ref	Width	Height	Sill	Head	Lintel
P3 dormitorio 1 (east)	3000	2800	+200	+3000	-
V5 landing (east)	930	1900	+4300	+6200	-

Structural openings in the ICF; sill and head above GF FFL.

WEST ELEVATION: OPENINGS

Ref	Width	Height	Sill	Head	Lintel
P1 entrance (west)	1680	2800	+200	+3000	-
V3 aseo (west)	600	2000	+1000	+3000	-

Structural openings in the ICF; sill and head above GF FFL.

EAST ELEVATION: LEVELS

Level	FFL
Plant room ICF base	-2743
Pool ICF base	-1829
U/S foundation ICF	-715
GF FFL	0
top of ICF	+3000
FF FFL	+3400
Solarium parapet	+4300
top of ICF	+6200
Roof	+6600
Parapet	+7000

WEST ELEVATION: LEVELS

Level	FFL
Plant room ICF base	-2743
Pool ICF base	-1829
U/S foundation ICF	-715
GF FFL	0
top of ICF	+3000
FF FFL	+3400
Solarium parapet	+4300
top of ICF	+6200
Roof	+6600
Parapet	+7000

NOTES

1. ICF: Nudura 6" XR35, 101.6 EPS + 152.4 core + 101.6 EPS = 355.6; 6" Std, 66.7 EPS + 152.4 core + 66.7 EPS = 285.8. External EPS face shown with the block course joints, vertical block joints and stack joints as populated.
2. Levels above GF FFL. Openings are structural openings in the ICF; glazing, doors, render and finishes by others, not shown.
3. Roof build-up shown as modelled.
4. See ES26-082-GA-01 for plan setting out, lintels and steel.

REVISIONS

REV	DATE	DESCRIPTION
Q01	19.10.26	First issue

Nudura™ BuildEase

CLIENT	PROJECT
Kume Arquitectura	Casa 7, Las Brenas, Lanzarote

DRAWING TITLE

EAST AND WEST ELEVATIONS

ICF elevations with openings, levels and roof build-up

SCALE	SIZE	DATE
1:150	A3	19.10.26
DRAWN	CHECKED	APPROVED
TS		

STATUS	DRAWING No.	REV
QUOTATION	ES26-082-EL-02	Q01